


Cellar Floor w/ Insul

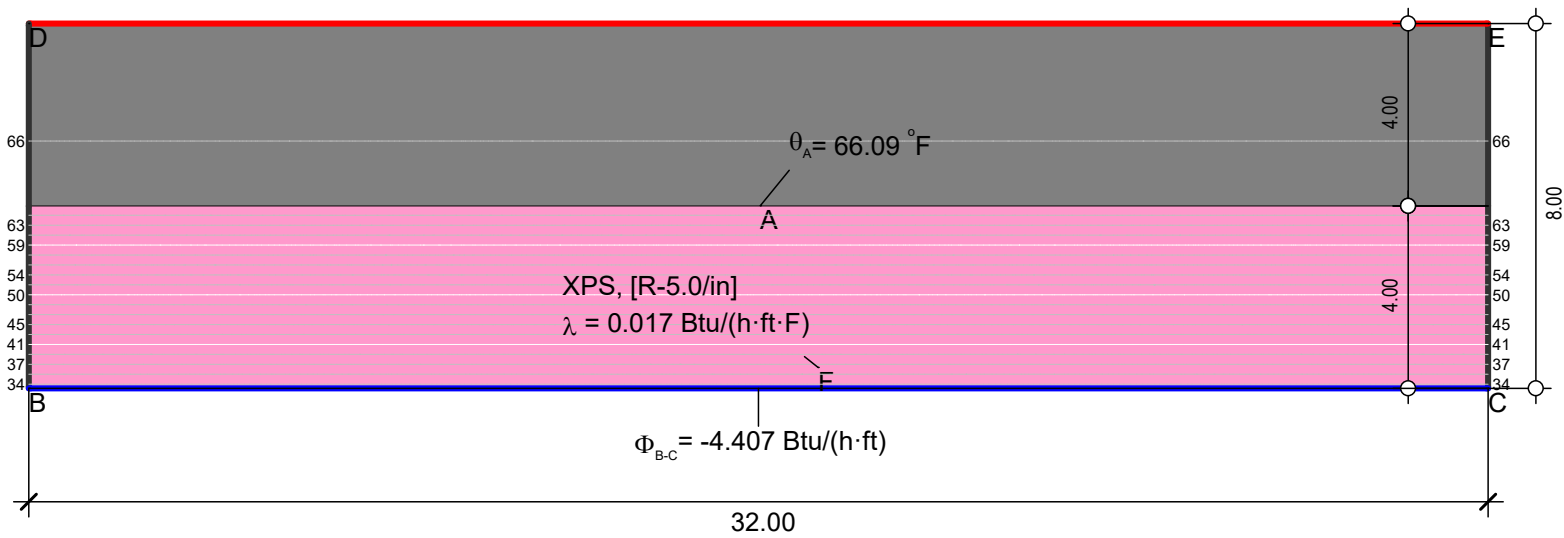

$$U_{eq\ B-C} = \frac{4.407}{36.18 \cdot 2.667} = 0.0457 \text{ Btu}/(\text{h}\cdot\text{ft}^2\cdot\text{F}) = R-21.8818$$

Boundary Condition	q[Btu/(h·ft²)]	θ[°F]	h[Btu/(h·ft²·F)]	ε
Exterior, Greenwich 90d Avg	31.820	1.355		
Interior, heat flux, downwards	68.000	1.036		
Symmetry/Model section	0.000			

Material	λ[Btu/(h·ft·F)]
Concrete (Heavily Reinforced) [R-0.05/in]	1.733
XPS, [R-5.0/in]	0.017