


Cellar Wall w/ Ext. Insul.

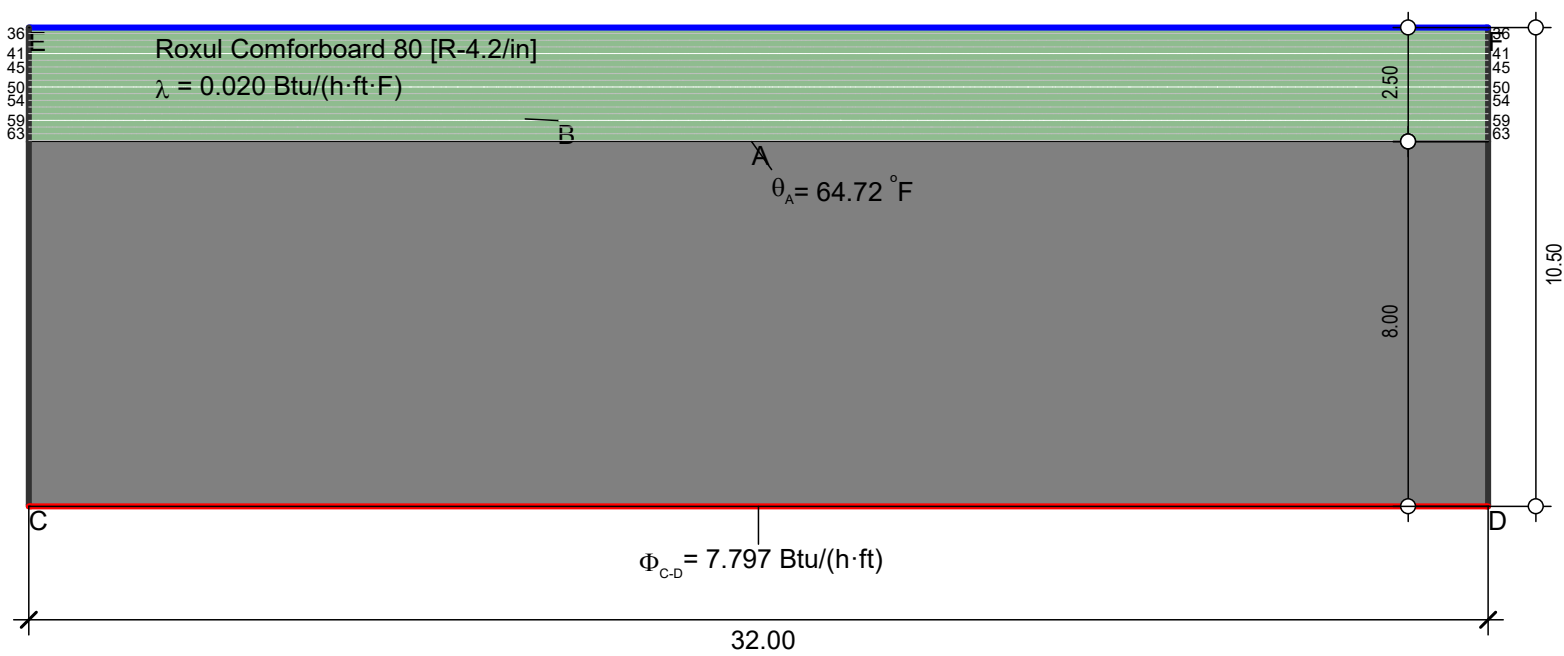

$$U_{eq\ C-D} = \frac{7.797}{36.18 \cdot 2.667} = 0.0808\ Btu/(h \cdot ft^2 \cdot F) = R-12.3762$$

Boundary Condition				Material	
q[Btu/(h·ft²)]	θ[°F]	h[Btu/(h·ft²·F)]	ε	λ[Btu/(h·ft·F)]	
Exterior, Greenwich 90d Avg	31.820	1.355		Concrete (Heavily Reinforced) [R-0.05/in]	1.733
Interior, normal, horizontal	68.000	1.355		Roxul Comforboard 80 [R-4.2/in]	0.020
Symmetry/Model section	0.000				