


Cellar Wall w/ Int. Insul.

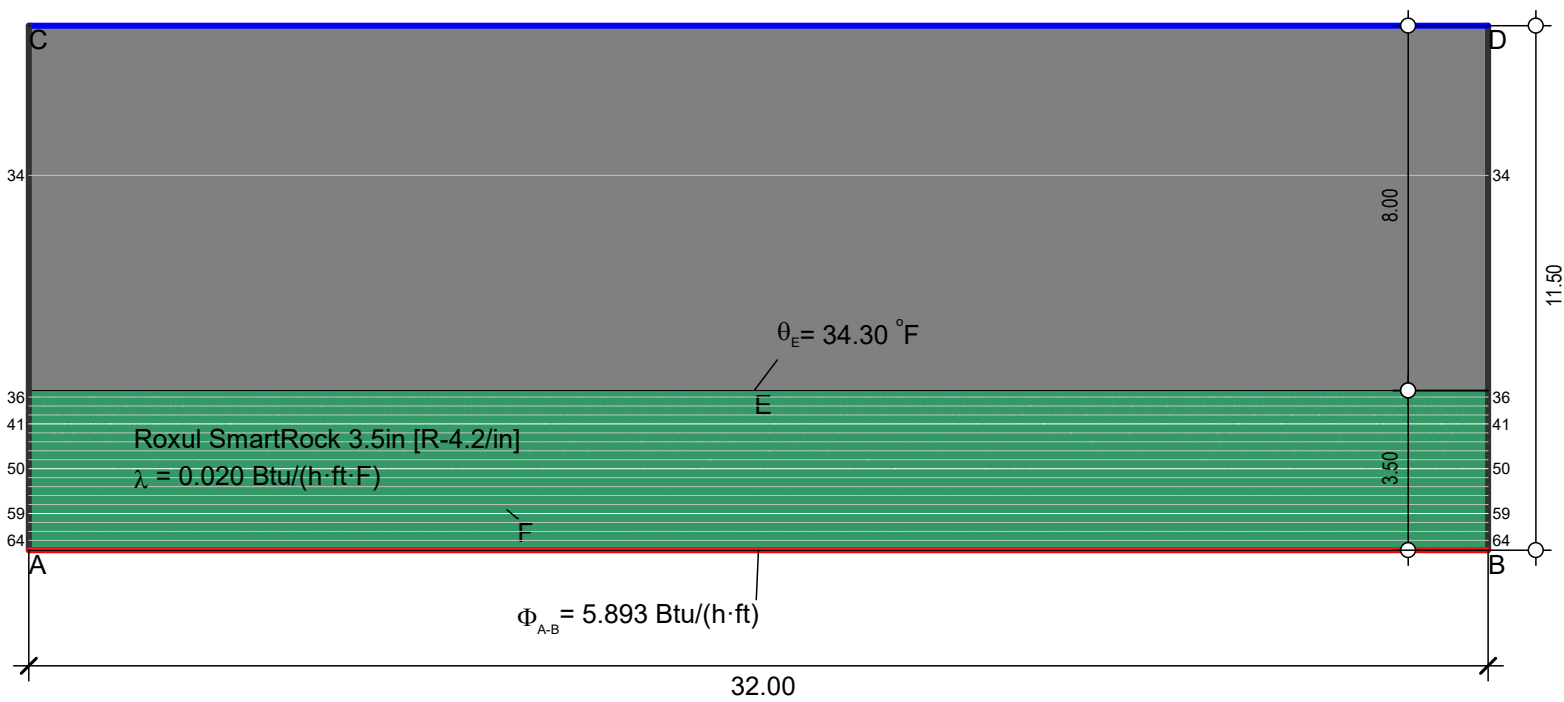

$$U_{eq\ A-B} = \frac{5.893}{36.18 \cdot 2.667} = 0.0611\ Btu/(h \cdot ft^2 \cdot F) = R-16.3666$$

Boundary Condition	q[Btu/(h·ft²)]	θ[°F]	h[Btu/(h·ft²·F)]	ε	Material	λ[Btu/(h·ft·F)]
Exterior, Greenwich 90d Avg		31.820	1.355		Concrete (Heavily Reinforced) [R-0.05/in]	1.733
Interior, normal, horizontal		68.000	1.355		Roxul SmartRock 3.5in [R-4.2/in]	0.020
Symmetry/Model section	0.000					