


Exterior Wall

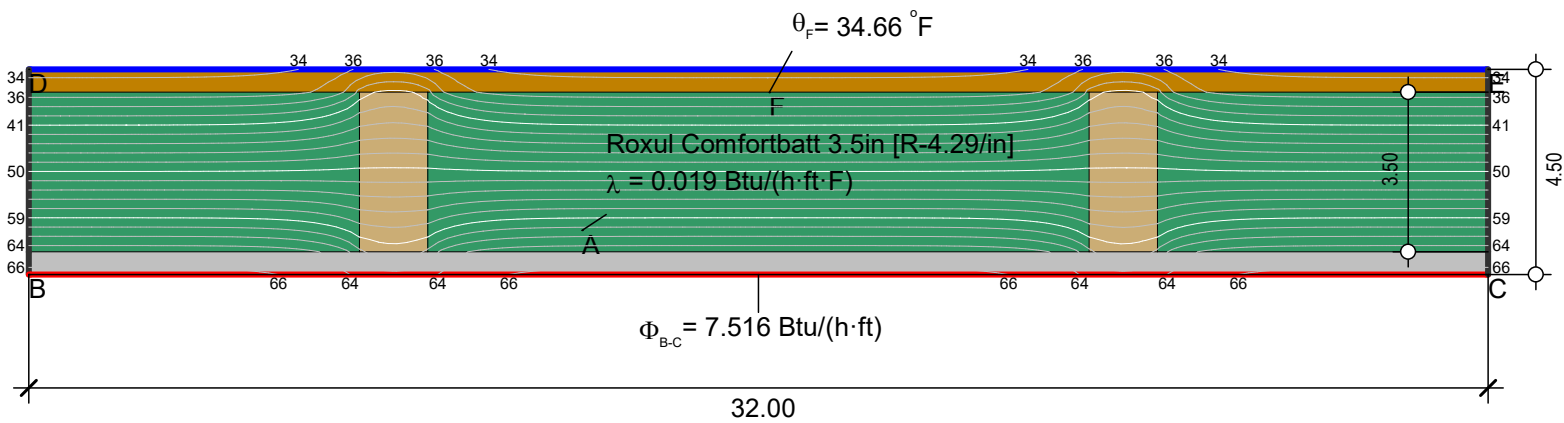

$$U_{eq\ B-C} = \frac{7.516}{36.18 \cdot 2.667} = 0.0779\ Btu/(h \cdot ft^2 \cdot F) = R-12.837$$

Boundary Condition				Material		$\lambda[Btu/(h \cdot ft \cdot F)]$
	$q[Btu/(h \cdot ft^2)]$	$\theta[^\circ F]$	$h[Btu/(h \cdot ft^2 \cdot F)]$	ε		
Exterior, Greenwich 90d Avg		31.820	1.355		GWB (Typ) [R-0.85/in]	0.098
Interior, normal, horizontal		68.000	1.355		Plywood (Typ) [R-1.2/in]	0.069
Symmetry/Model section	0.000				Roxul Comfortbatt 3.5in [R-4.29/in]	0.019
					Wood, Coniferous [550 kg/m3], grain vertical	0.071, 0.161