


Exterior Wall w/ Insul.

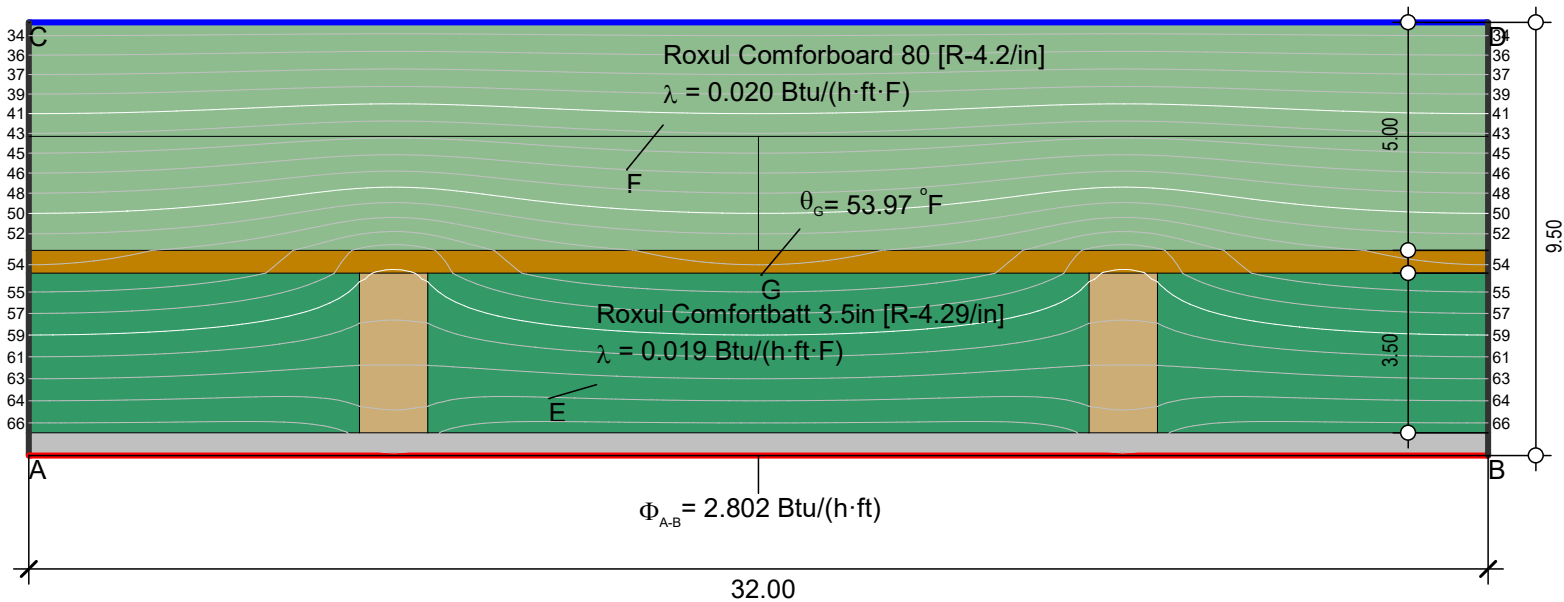

$$U_{eq\ A-B} = \frac{2.802}{36.18 \cdot 2.667} = 0.0290\ Btu/(h \cdot ft^2 \cdot F) = R-34.4828$$

Boundary Condition				Material	$\lambda[Btu/(h \cdot ft \cdot F)]$
	$q[Btu/(h \cdot ft^2)]$	$\theta[^\circ F]$	$h[Btu/(h \cdot ft^2 \cdot F)]$	ε	
Exterior, Greenwich 90d Avg	31.820	31.820	1.355	GWB (Typ) [R-0.85/in]	0.098
Interior, normal, horizontal	68.000	68.000	1.355	Plywood (Typ) [R-1.2/in]	0.069
Symmetry/Model section	0.000			Roxul Comforboard 80 [R-4.2/in]	0.020
				Roxul Comfortbatt 3.5in [R-4.29/in]	0.019
				Wood, Coniferous [550 kg/m³], grain vertical	0.071, 0.161