


Flat Roof

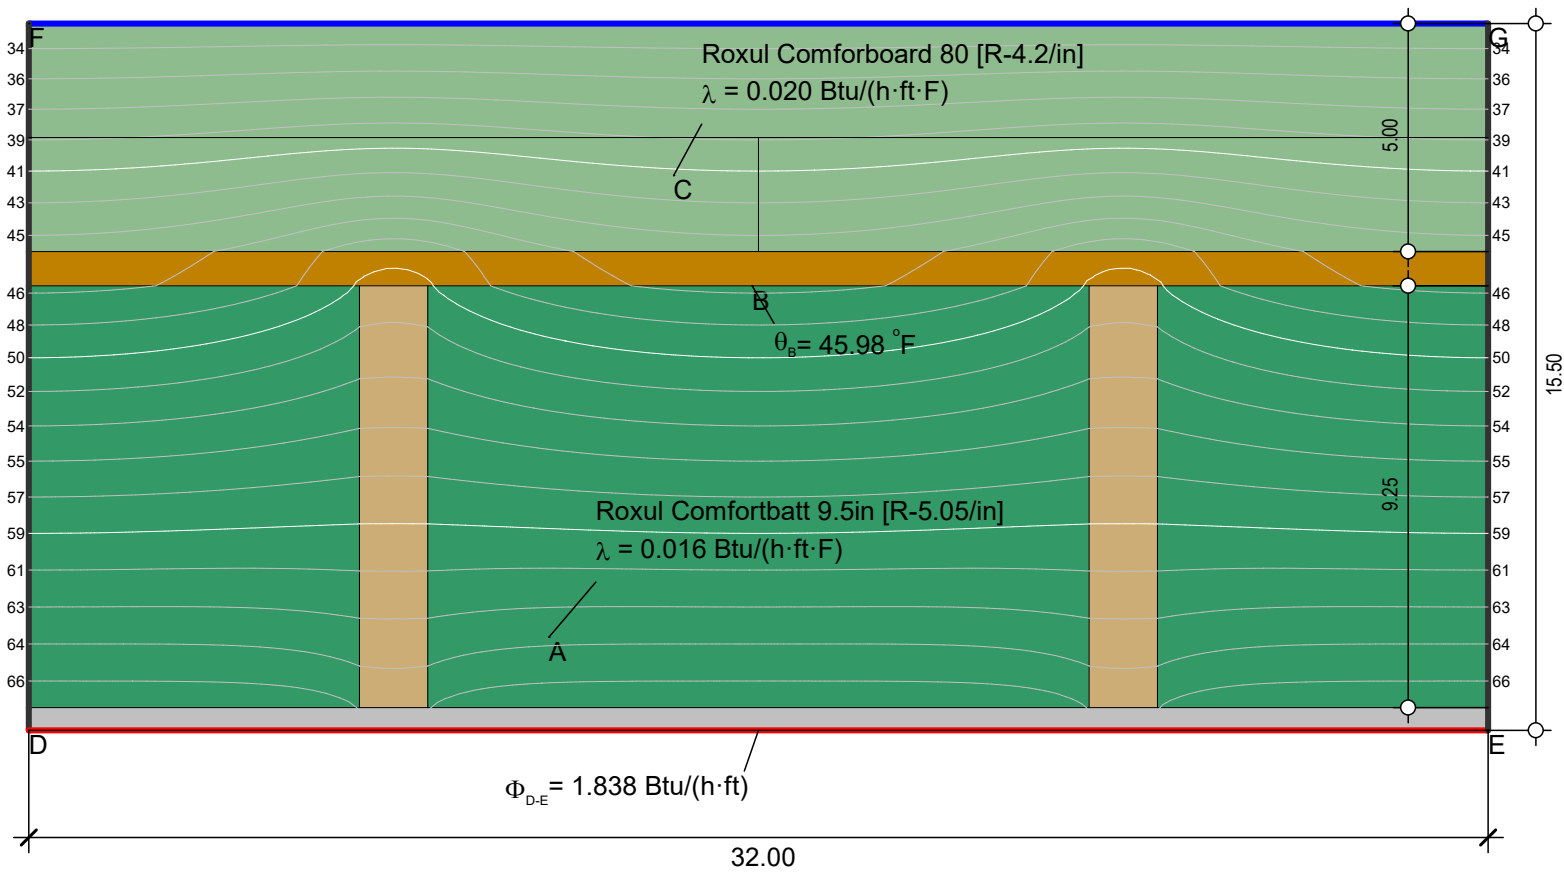

$$U_{eq\ D-E} = \frac{1.838}{36.18 \cdot 2.667} = 0.0190\ Btu/(h \cdot ft^2 \cdot F) = R-49.7512$$

Boundary Condition				Material	$\lambda[Btu/(h \cdot ft \cdot F)]$
	$q[Btu/(h \cdot ft^2)]$	$\theta[^\circ F]$	$h[Btu/(h \cdot ft^2 \cdot F)]$		
Exterior, Greenwich 90d Avg		31.820	1.355	GWB (Typ) [R-0.85/in]	0.098
Interior, normal, horizontal		68.000	1.355	Plywood (Typ) [R-1.2/in]	0.069
Symmetry/Model section	0.000			Roxul Comforboard 80 [R-4.2/in]	0.020
				Roxul Comfortbatt 9.5in [R-5.05/in]	0.016
				Wood, Coniferous [550 kg/m3], grain vertical	0.071, 0.161