


Garage Ceiling

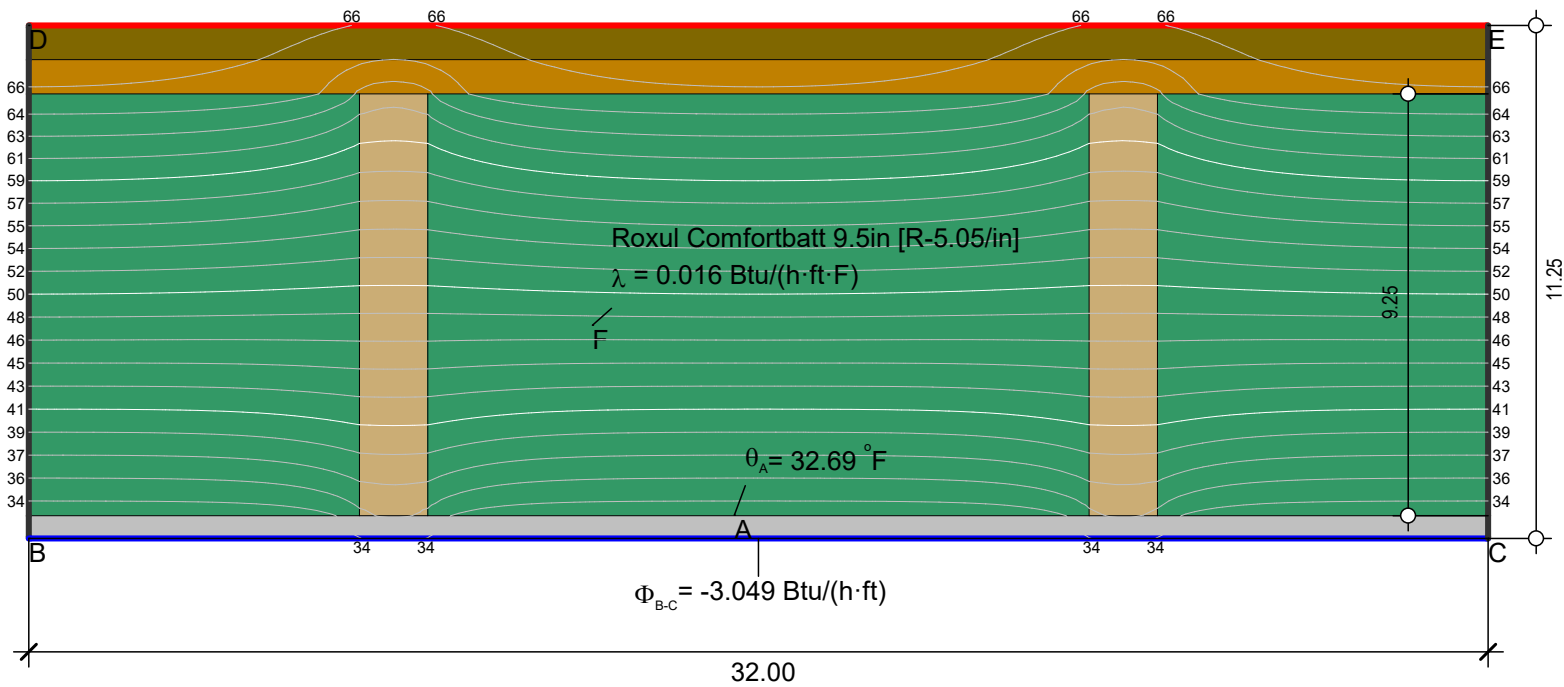

$$U_{eq\ B-C} = \frac{3.049}{36.18 \cdot 2.667} = 0.0316\ Btu/(h \cdot ft^2 \cdot F) = R-31.6456$$

Boundary Condition					Material	λ[Btu/(h·ft·F)]
q[Btu/(h·ft ²)]	θ[°F]	h[Btu/(h·ft ² ·F)]	ε			
Exterior, Greenwich 90d Avg	31.820	1.355			GWB (Typ) [R-0.85/in]	0.098
Interior, heat flux, downwards	68.000	1.036			Plywood (Typ) [R-1.2/in]	0.069
Symmetry/Model section	0.000				Roxul Comfortbatt 9.5in [R-5.05/in]	0.016
					Wood, Coniferous [550 kg/m3], grain vertical	0.071, 0.161
					Wood, Deciduous (Hardwood) [R-0.91/in]	0.092