


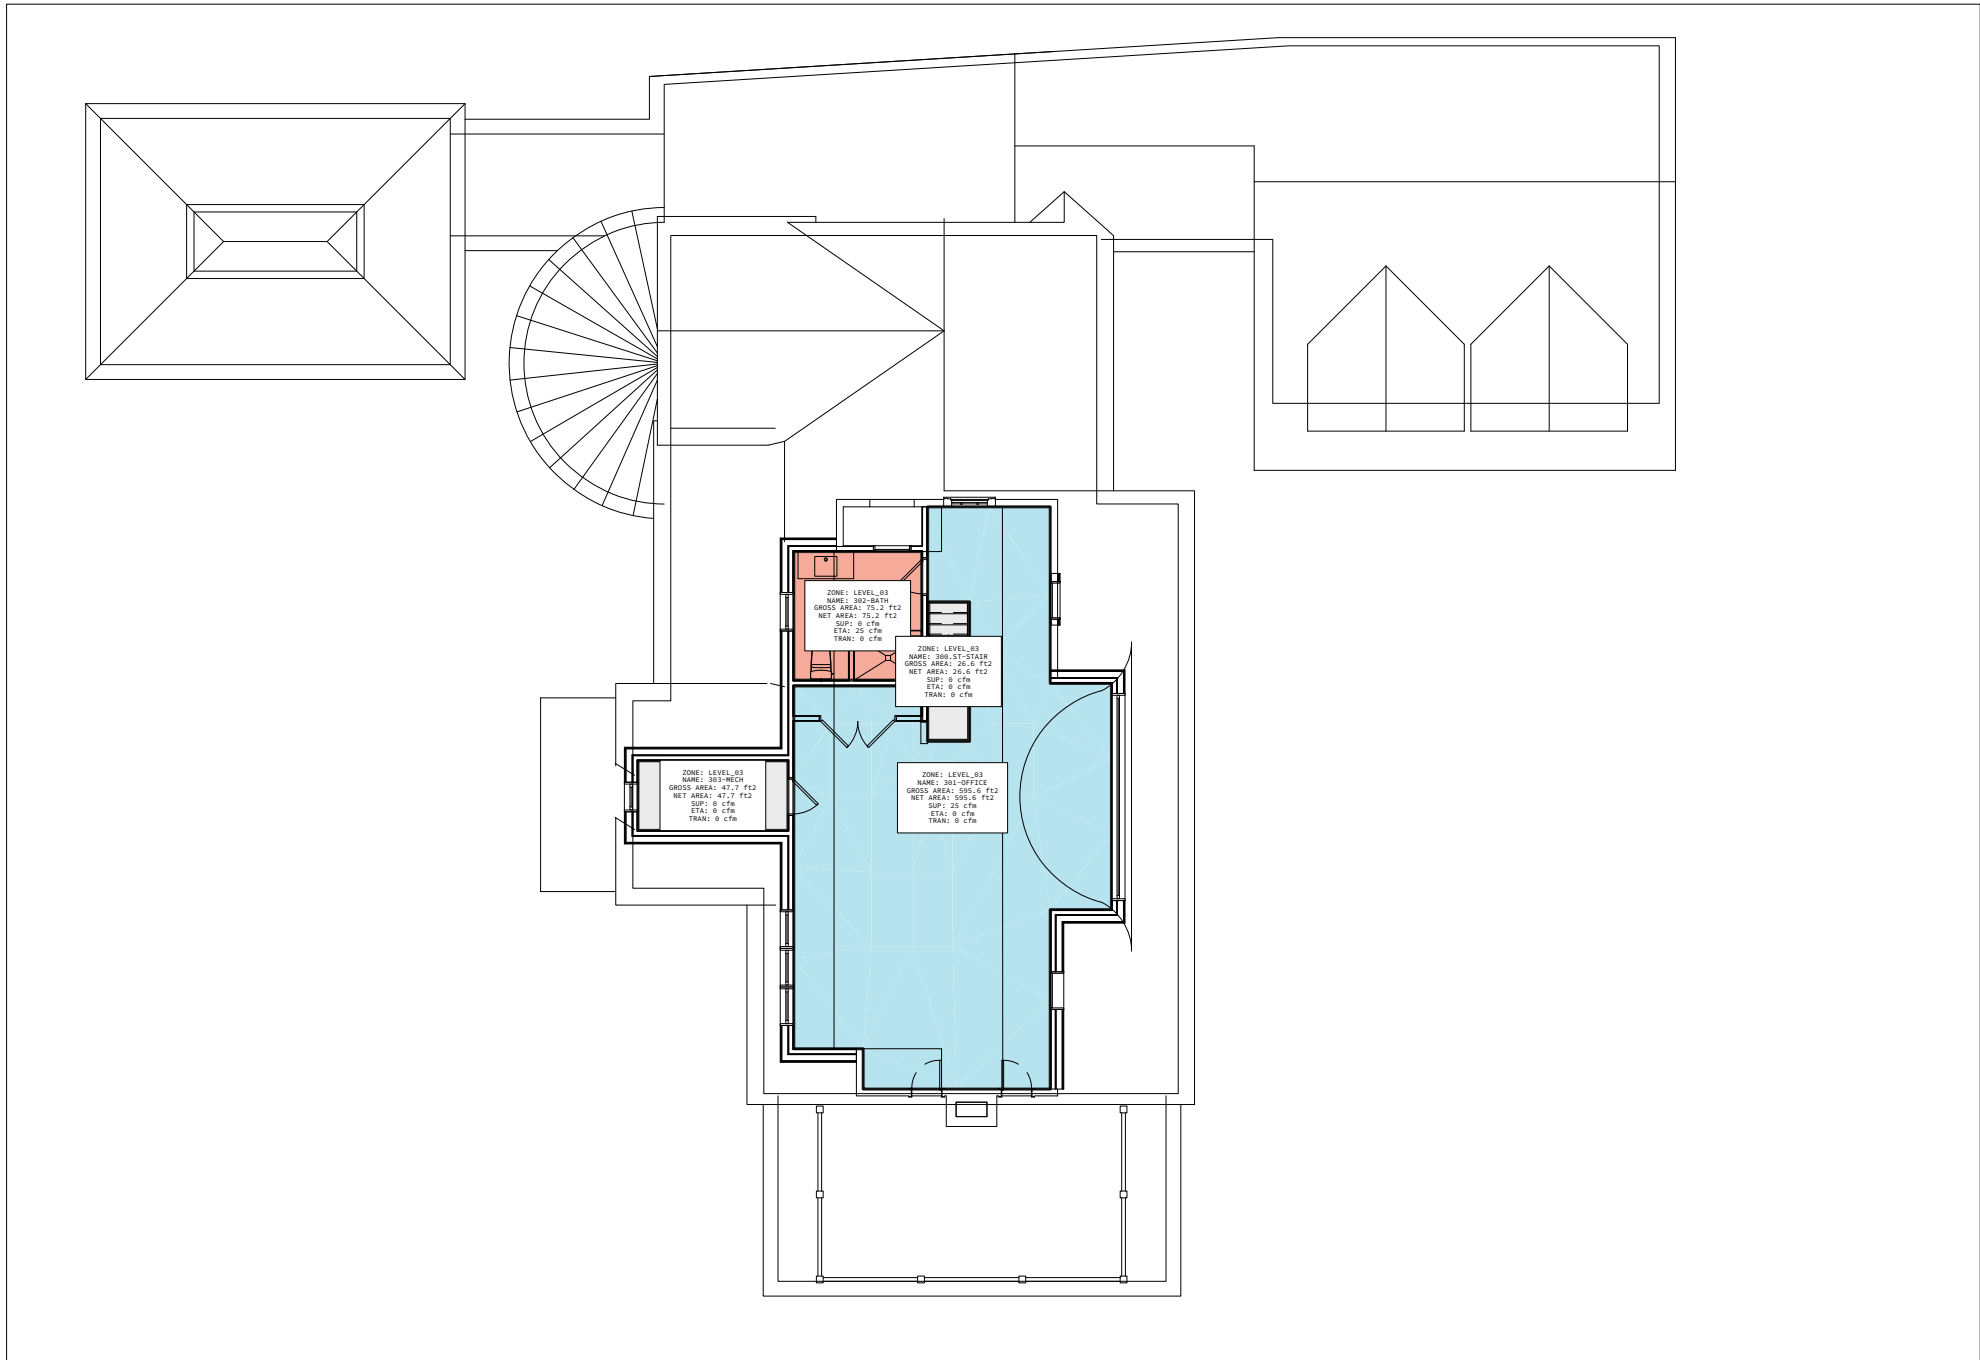

INDIAN HEAD RD. HOME

FRESH-AIR VENTILATION PLANS

Ventilation:

SUPPLY

EXTRACT

SUP & ETA